

 Kamera DS-2CD2643G2-IZS


okablowanie miedziane

— okablowanie światłowodowe

230V^o istniejący punkt zasilania w słupie

1xPoe OUT,
1xSFP

Media Converter - 1xPoE OUT,
1xSFP

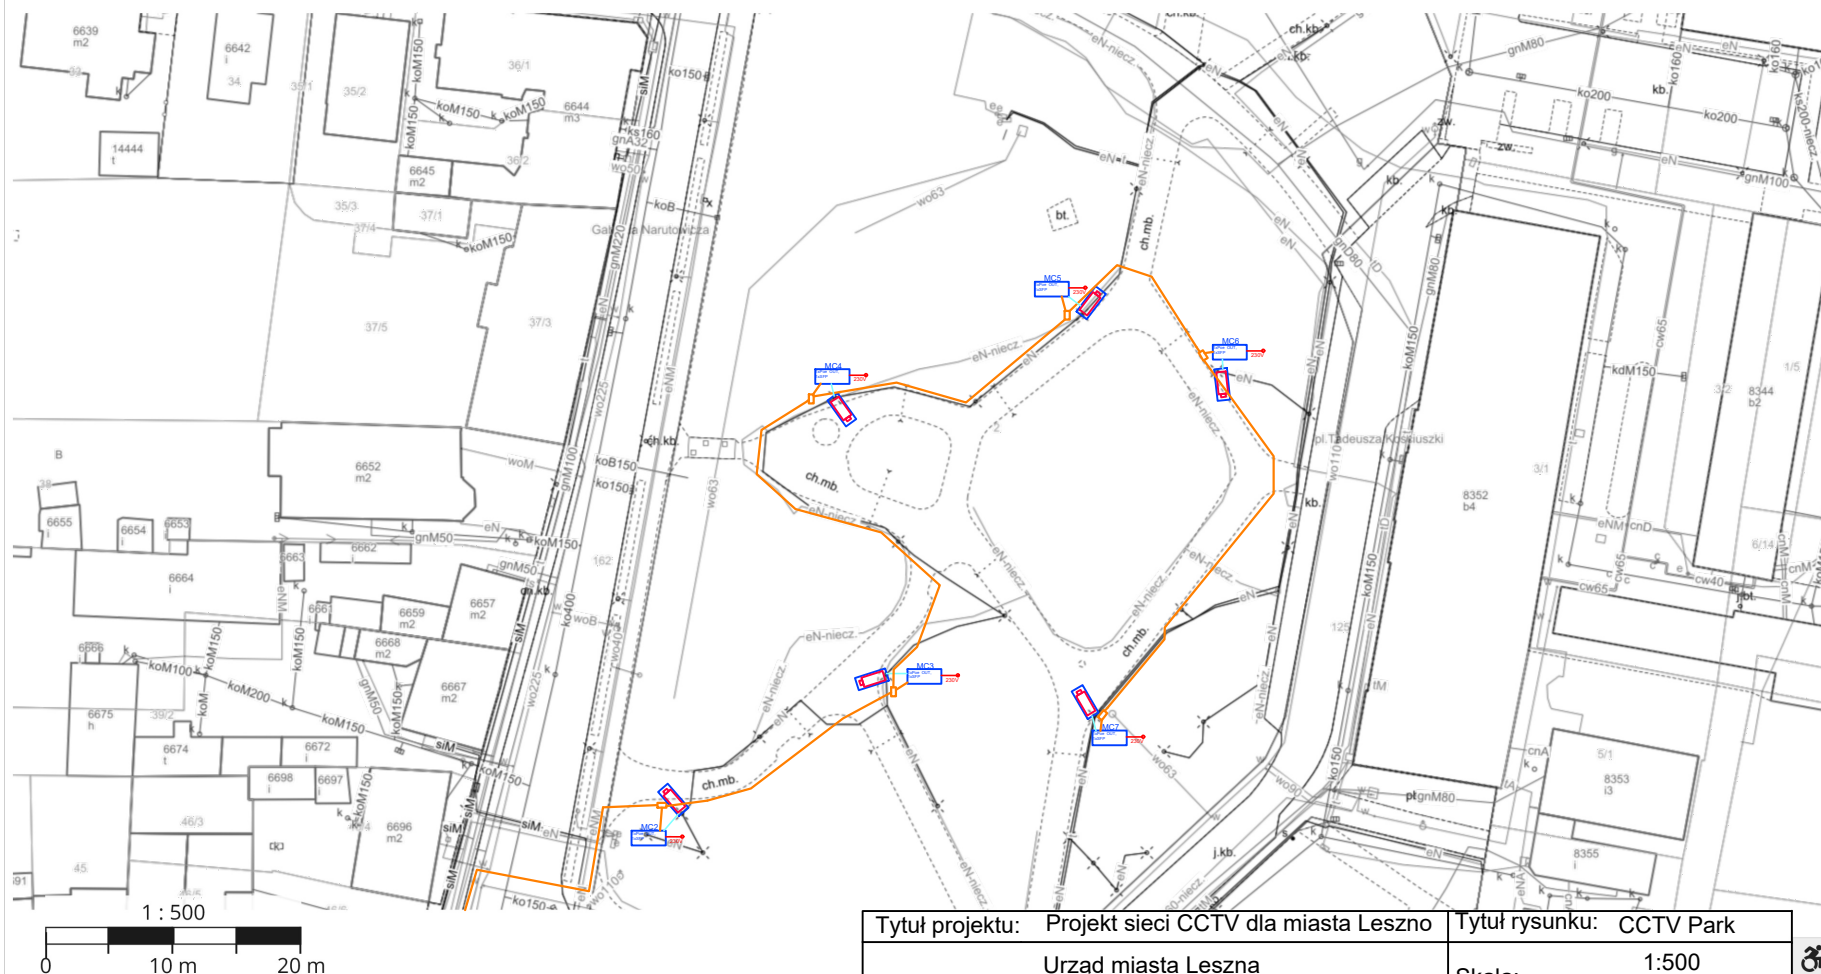

Tytuł projektu:	Projekt sieci CCTV dla miasta Leszno	Tytuł rysunku:	CCTV Park
Inwestor:	Urząd miasta Leszna Kazimierza Karasia 15 64-100 Leszno	Skala:	1:500 A4
Projektant:	Aleks Kusztelak 273056	Data:	06.2025
		Podpis:	