

Legenda

-  Kamera DS-2CD2643G2-IZS
 Kamera IDS-2CD7A46GO/P-IZHSY(8-32MM)

 okablowanie miedziane

 okablowanie światłowodowe

 230V istniejący punkt zasilania w słupie

PD1-2


5xPoe, 1xUplink,
1xMedia
converter IN

Punkt dostępowy - Switch 5xP+1UP
oraz MC IN

MC1

1xPoe OUT,
1xSFP

Media Converter - 1xPoe OUT,
1xSFP

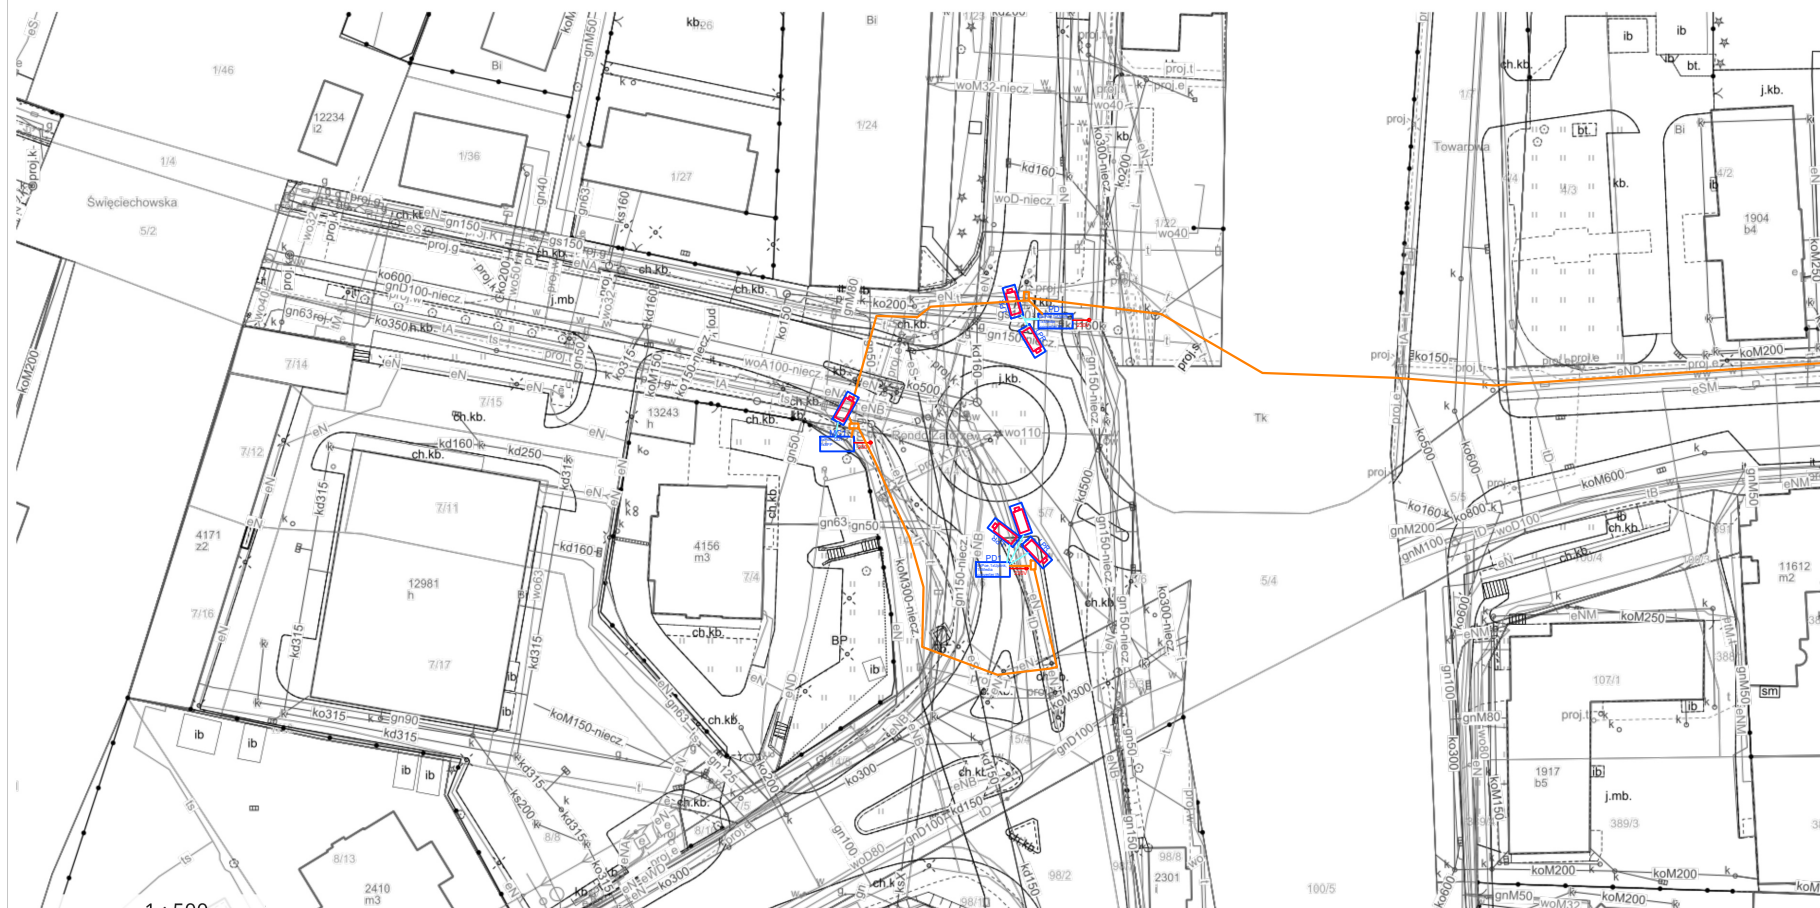

1 : 500
0 10 m 20 m

Tytuł projektu: Projekt sieci CCTV dla miasta Leszno

Tytuł rysunku: CCTV Rondo

Inwestor:  Urząd miasta Leszno
Kazimierza Karasia 15
64-100 Leszno

Skala: 1:500
A4

Projektant: Aleks Kusztelek
273056

Data: 06.2025

Podpis:

